


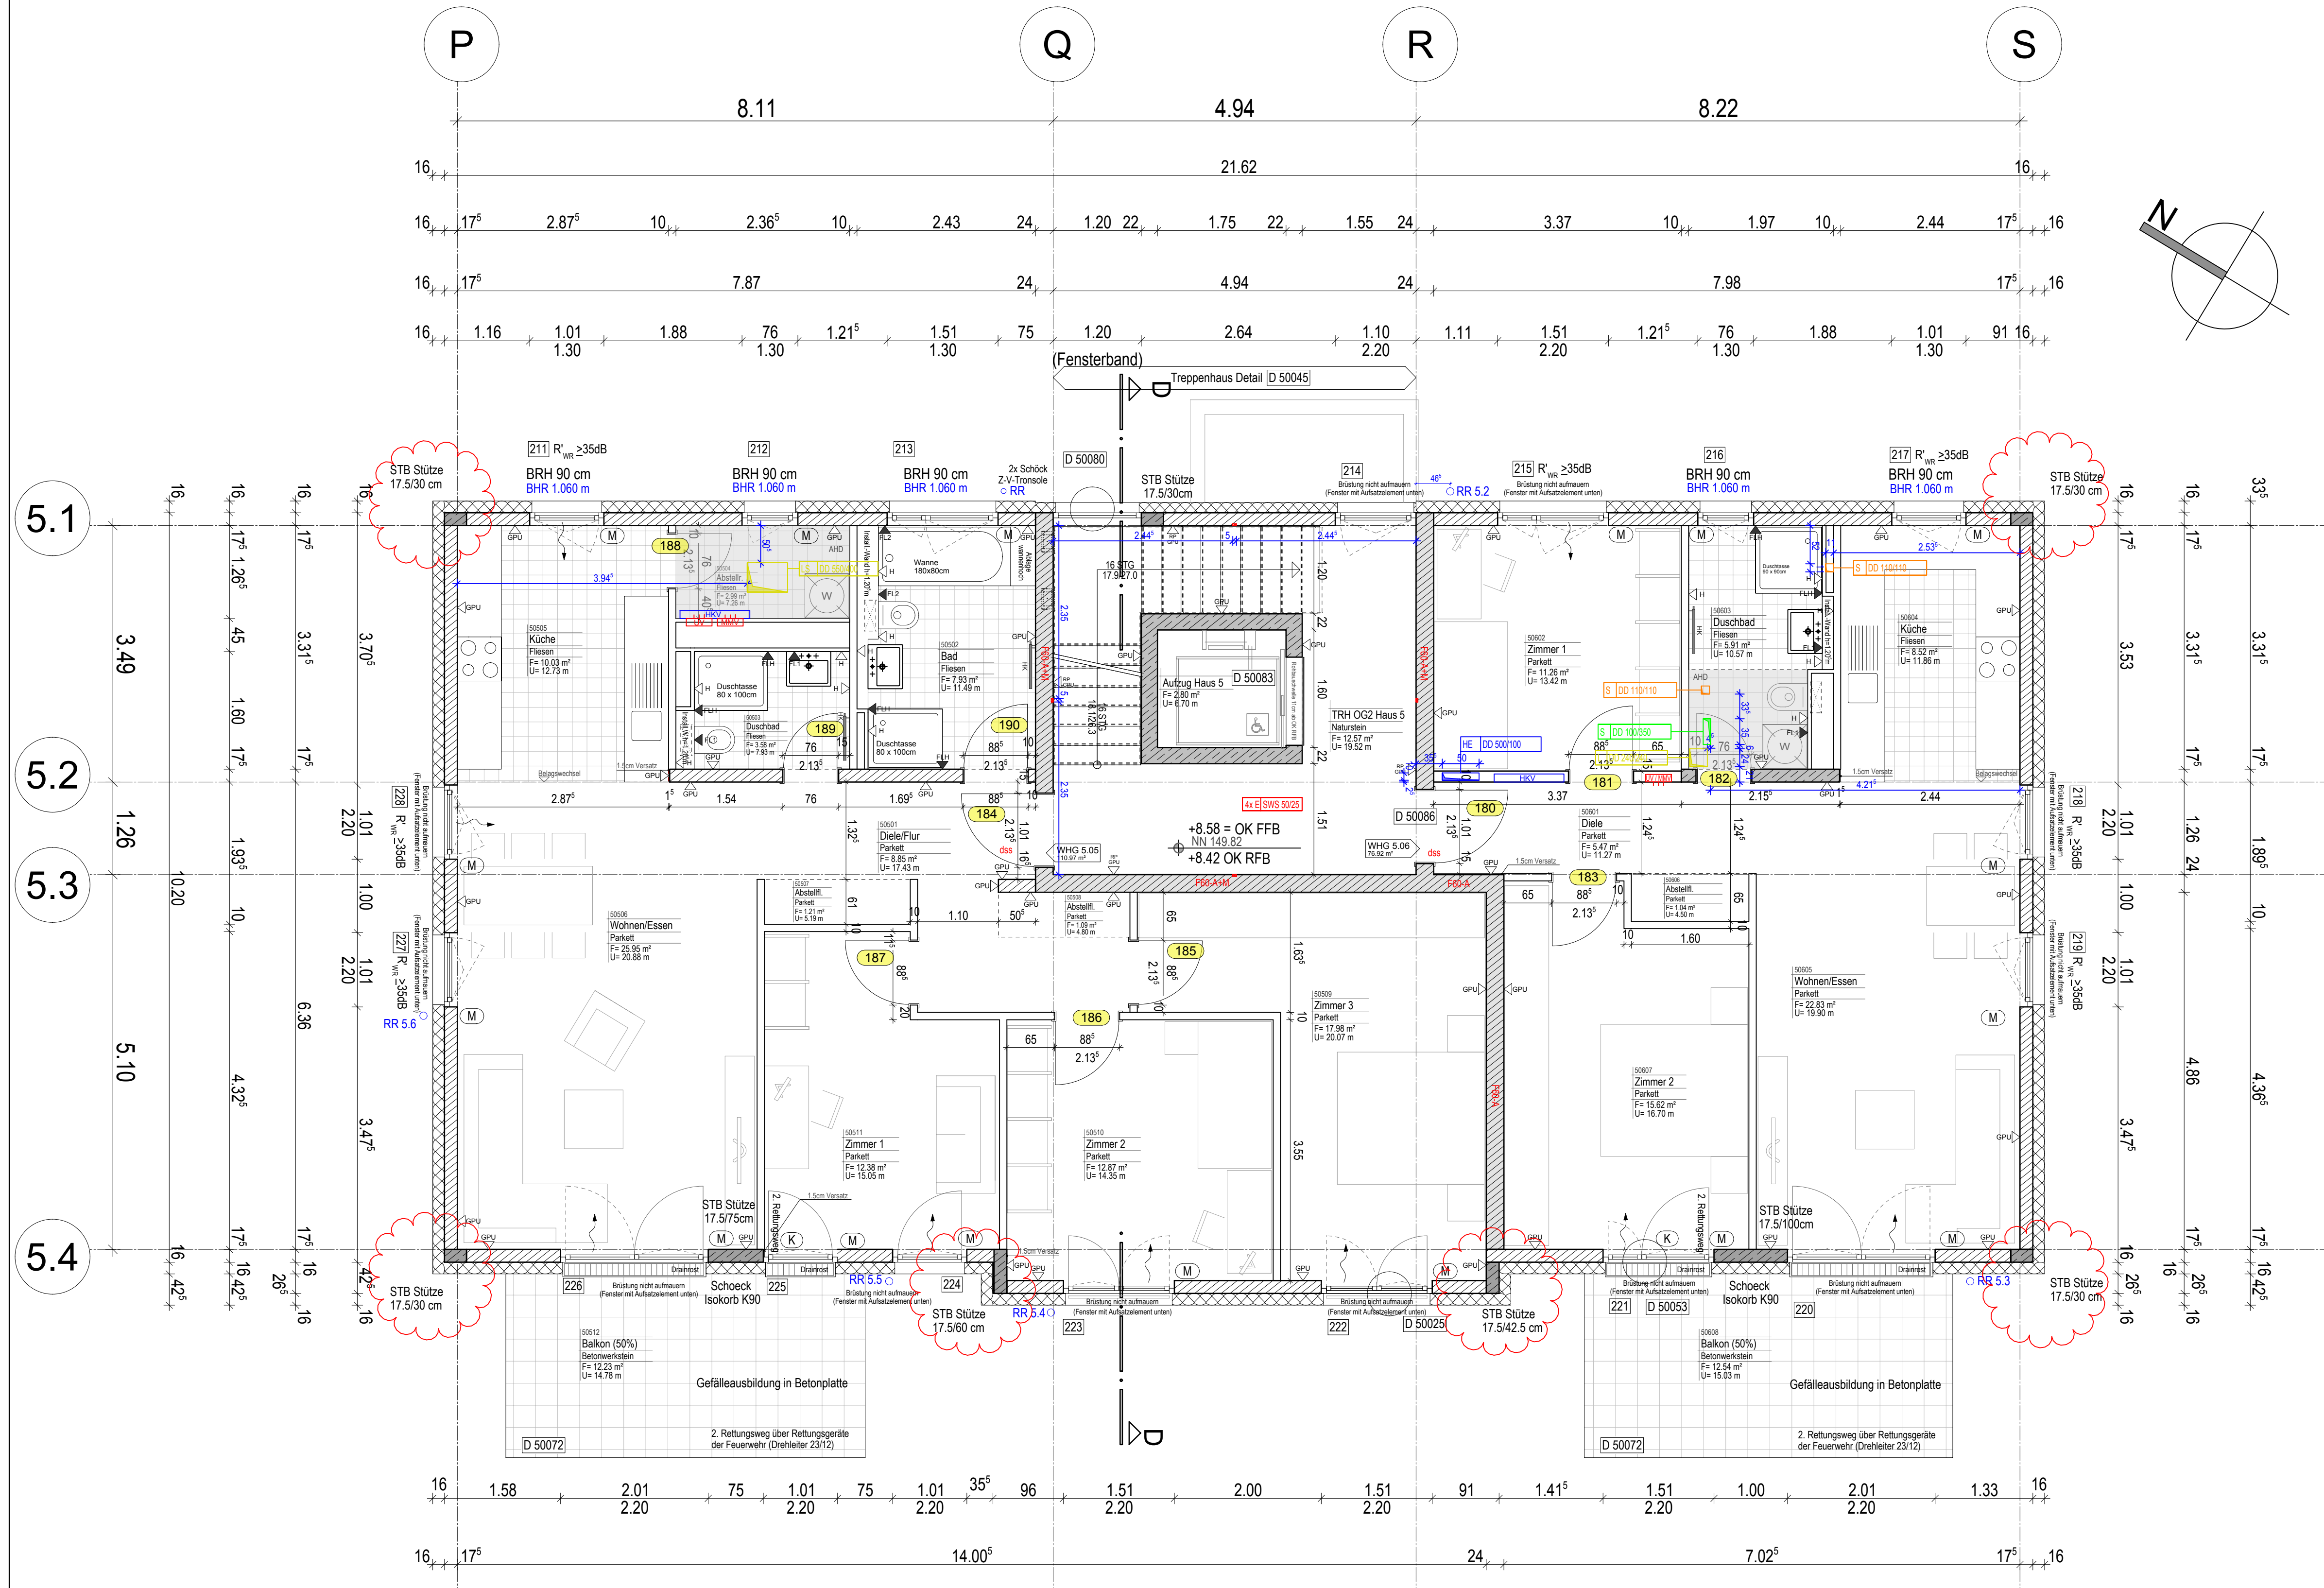

Legende:

- Höhenkote
- OK Oberkante
- UK Unterkante
- VK Vorderkante
- RFB Rohfußboden
- FFB Fertigfußboden
- BRH Brüstungshöhe von FFB bis OK Brüstung roh
- BHR Brüstungshöhe roh von RFB bis OK Brüstung roh
- WS Wandschlitz
- WD Wanddurchbruch
- DD Deckendurchbruch
- BD Bodendurchbruch
- BS Bodenschlitz
- BK Bodenkanal
- RWA Rauchwärmeabzug
- RA Rauchabzug
- F30 feuerhemmend W30 T30 G30
- F90 feuerbeständig W90 T90 G90
- RS Rauchschutz Türen
- dss dicht und selbstschließende Türen
- D 50002 Detailverweis
- HK Heizkörper
- H Heizung
- L Lüftung
- E Elektro
- S Sanitär
- RR Regenfallrohr
- BE Bodenablauf
- Heizkreisverteiler
- Multimedienverteiler
- Elektroverteilung
- Lage des Rollladenantriebes max. Behangbreite 2,70m pro Behang eigener Antrieb
- Kurbelantrieb in Laibung für 2. Rettungsweg
- = Fensternummerierung
- = Türnummerierung
- ALU
- Fassade
- Schlosser
- Tischler
- Außenluftdurchlass System Aereco innenseitig auf Fensterflügel montiert
- Gipskarton, hydrophobiert
- Gipsputz
- Gipsspachtelputz
- Gipsspachtelputz + Reibputz
- Fliessen h = 1.20 m
- Fliessen h = 1.50 m
- Fliessen raumhoch
- Wandtypen:**
- Stahlbeton
- Mauerwerk in Brandschutzqualität
- Gipskarton-Ständerwand
- Mauerwerk KS 20
- Mauerwerk KS-L 12

Alle Fenster- und Türhöhen beziehen sich auf OKFFB !!!

Alle Maße sind am Bau zu Prüfen Unstimmigkeiten sind sofort mit der Bauleitung abzuklären

Für den Planinhalt hinsichtlich DD/BD und WD der Gewerke H/L/S/TW/E ist der beauftragte Fachingenieur Ing.-Büro Horn verantwortlich !

	KD	28.05.18	I
Stahlbetonstützen in Außenwand ergänzt	KD	28.05.18	I
Stahlbetonstützen in Wand Achse (5.2) entfällt	KD	16.05.18	H
Abgleich/Optimierung der ALDs	KD	06.04.18	G
NU-Freigabe	KD	15.02.18	F
Maße ergänzt	KD	24.01.18	E
Plantyp WP3, Tür verschoben, Handtuchheizkörper ergänzt	KD	21.12.17	D
ÄNDERUNG	GEZ.	DATUM	IND.

Rebstock QUARTIER Bad Kreuznach

Haus 1+2 Haus 3+4 Haus 5

Bauvorhaben Neubau von 5 Mehrfamilienhäusern mit TG Pappelweg 1-9, Bad Kreuznach

Zeichnung Grundriss 2.Obergeschoss Haus 5 **Maßstab:** 1:50 **gez.** KD

Plan-Nr. 70675-ARC-50012-F-I-A-GR-OG2-H05

Datum 28.05.2018 **Projektnr.** 0.675.00

WP3

Bauherr Wilma Wohnen Süd RM GmbH Kuhwaldstraße 46 60486 Frankfurt am Main Tel: 069 - 58 00 74 - 0

Entwurfsverfasser projekt62 **architekten + ingenieure** **Wilma**

Unterschrift

Unterschrift