

Einheit 17
22.23 m²

H1 - 2.OG	H1 - 2.OG
17.Zimmer	17.Bad
GFL 16.74 m²	GFL 2.97 m²
WFL 16.85 m²	WFL 2.88 m²
UMF 20.54 m	UMF 7.18 m
Boden: Linoleum	Boden: BB-FLIESEN1\
Decke: DB-ANSTRICH\	Decke: DB-ANSTRICH\
Wand: WB-ANSTRICH1\	Wand: WB-ANSTRICH1\

H1 - 2.OG	H1 - 2.OG
17.Balkon	
GFL 4.34 m²	
WFL 2.17 m²	
UMF 9.00 m	
Boden: BB-BESCHÜTTUNG1\	
Decke:	
Wand:	

Einheit 18
22.93 m²

H1 - 2.OG	H1 - 2.OG
18.Zimmer	18.Bad
GFL 17.37 m²	GFL 2.97 m²
WFL 17.37 m²	WFL 2.88 m²
UMF 20.72 m	UMF 7.18 m
Boden: Linoleum	Boden: BB-FLIESEN1\
Decke: DB-ANSTRICH\	Decke: DB-ANSTRICH\
Wand: WB-ANSTRICH1\	Wand: WB-ANSTRICH1\

H1 - 2.OG	H1 - 2.OG
18.Balkon	
GFL 4.67 m²	
WFL 2.34 m²	
UMF 9.49 m	
Boden: BB-BESCHÜTTUNG1\	
Decke:	
Wand:	

Einheit 19
24.18 m²

H1 - 2.OG	H1 - 2.OG
19.Zimmer	19.Bad
GFL 18.62 m²	GFL 2.97 m²
WFL 18.62 m²	WFL 2.88 m²
UMF 20.99 m	UMF 7.18 m
Boden: Linoleum	Boden: BB-FLIESEN1\
Decke: DB-ANSTRICH\	Decke: DB-ANSTRICH\
Wand: WB-ANSTRICH1\	Wand: WB-ANSTRICH1\


H1 - 2.OG	H1 - 2.OG
19.Balkon	
GFL 4.67 m²	
WFL 2.34 m²	
UMF 9.48 m	
Boden: BB-BESCHÜTTUNG1\	
Decke:	
Wand:	

Einheit 20
44.46 m²

H1 - 2.OG	H1 - 2.OG
20.1.Zimmer	20.2.Zimmer
GFL 14.20 m²	GFL 13.54 m²
WFL 14.26 m²	WFL 13.71 m²
UMF 15.99 m	UMF 15.38 m
Boden: Linoleum	Boden: Linoleum
Decke: DB-ANSTRICH\	Decke: DB-ANSTRICH\
Wand: WB-ANSTRICH1\	Wand: WB-ANSTRICH1\

H1 - 2.OG	H1 - 2.OG
20.1.Balkon	20.2.Balkon
GFL 4.67 m²	GFL 4.34 m²
WFL 2.34 m²	WFL 2.17 m²
UMF 9.48 m	UMF 9.01 m
Boden: BB-BESCHÜTTUNG1\	Boden: BB-BESCHÜTTUNG1\
Decke:	Decke:
Wand:	Wand:

H1 - 2.OG	H1 - 2.OG
20.Küche/Flur	20.Bad_Barrierefrei
GFL 7.72 m²	GFL 3.79 m²
WFL 7.67 m²	WFL 3.69 m²
UMF 11.93 m	UMF 8.13 m
Boden: Linoleum	Boden: Linoleum
Decke: DB-ANSTRICH\	Decke: DB-ANSTRICH\
Wand: WB-ANSTRICH1\	Wand: WB-ANSTRICH1\

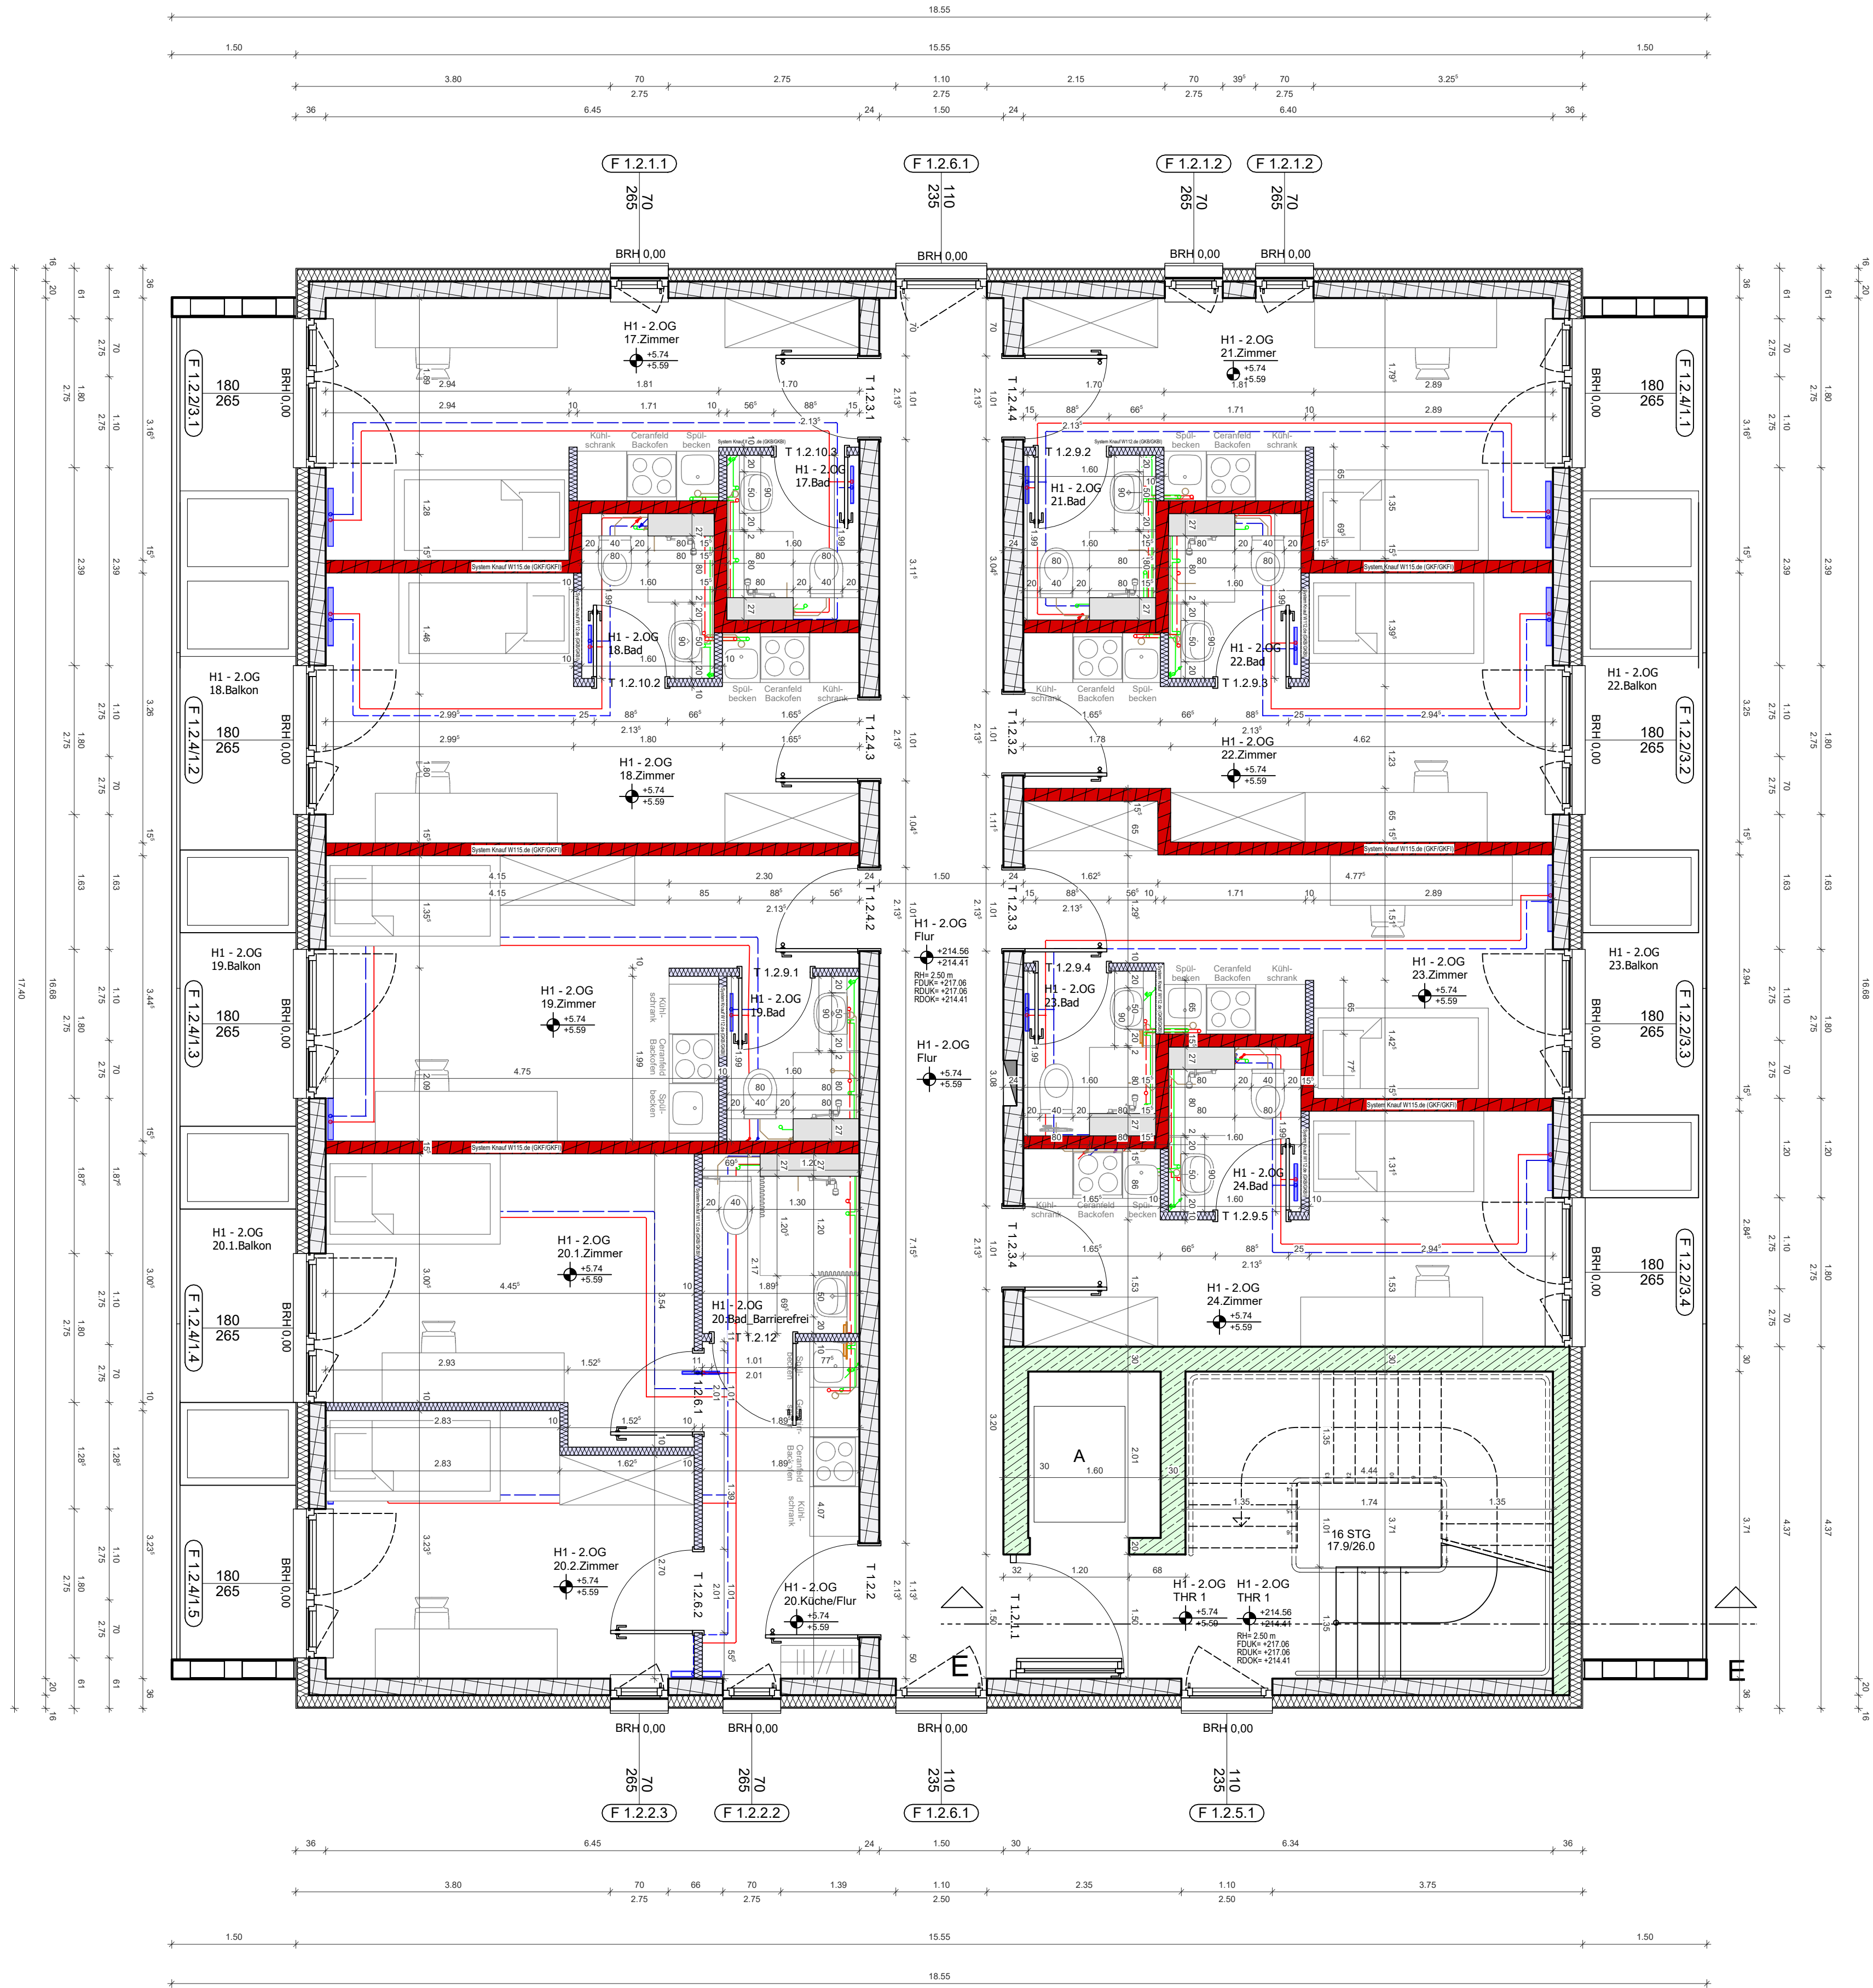

Einheit 21
22.17 m²

H1 - 2.OG	H1 - 2.OG
21.Zimmer	21.Bad
GFL 16.58 m²	GFL 2.97 m²
WFL 16.80 m²	WFL 2.88 m²
UMF 20.44 m	UMF 7.18 m
Boden: Linoleum	Boden: BB-FLIESEN1\
Decke: DB-ANSTRICH\	Decke: DB-ANSTRICH\
Wand: WB-ANSTRICH1\	Wand: WB-ANSTRICH1\

H1 - 2.OG	H1 - 2.OG
21.Balkon	
GFL 4.34 m²	
WFL 2.17 m²	
UMF 9.00 m	
Boden: BB-BESCHÜTTUNG1\	
Decke:	
Wand:	

Einheit 22
21.53 m²

H1 - 2.OG	H1 - 2.OG
22.Zimmer	22.Bad
GFL 15.98 m²	GFL 2.97 m²
WFL 15.98 m²	WFL 2.88 m²
UMF 20.60 m	UMF 7.18 m
Boden: Linoleum	Boden: BB-FLIESEN1\
Decke: DB-ANSTRICH\	Decke: DB-ANSTRICH\
Wand: WB-ANSTRICH1\	Wand: WB-ANSTRICH1\

H1 - 2.OG	H1 - 2.OG
22.Balkon	
GFL 4.67 m²	
WFL 2.33 m²	
UMF 9.48 m	
Boden: BB-BESCHÜTTUNG1\	
Decke:	
Wand:	

Einheit 23
21.09 m²

H1 - 2.OG	H1 - 2.OG
23.Zimmer	23.Bad
GFL 15.63 m²	GFL 2.97 m²
WFL 15.62 m²	WFL 2.88 m²
UMF 21.28 m	UMF 7.18 m
Boden: Linoleum	Boden: BB-FLIESEN1\
Decke: DB-ANSTRICH\	Decke: DB-ANSTRICH\
Wand: WB-ANSTRICH1\	Wand: WB-ANSTRICH1\

H1 - 2.OG	H1 - 2.OG
23.Balkon	
GFL 4.48 m²	
WFL 2.24 m²	
UMF 9.20 m	
Boden: BB-BESCHÜTTUNG1\	
Decke:	
Wand:	

Einheit 24
22.92 m²

H1 - 2.OG	H1 - 2.OG
24.Zimmer	24.Bad
GFL 15.10 m²	GFL 2.97 m²
WFL 15.11 m²	WFL 2.88 m²
UMF 20.21 m	UMF 7.18 m
Boden: Linoleum	Boden: BB-FLIESEN1\
Decke: DB-ANSTRICH\	Decke: DB-ANSTRICH\
Wand: WB-ANSTRICH1\	Wand: WB-ANSTRICH1\

H1 - 2.OG	H1 - 2.OG
24.Balkon	
GFL 9.21 m²	
WFL 4.60 m²	
UMF 15.95 m	
Boden: BB-BESCHÜTTUNG1\	
Decke:	
Wand:	

H1 - 2.OG	H1 - 2.OG
Flur	THR 1
GFL 25.02 m²	GFL 17.65 m²
WFL 24.86 m²	WFL 17.41 m²
UMF 36.36 m	UMF 25.72 m
Boden: BB-BESCHÜTTUNG1\	Boden: BB-BESCHÜTTUNG1\
Decke: DB-ANSTRICH\	Decke: DB-ANSTRICH\
Wand: WB-ANSTRICH1\	Wand: WB-ANSTRICH1\

LEGENDE

Kalksandsteinmauerwerk	UK	Unterkannte
Ortbeton bewehrt	OK	Oberkannte
Trockenbau	RFB	Fertigfußboden
F90 Trockenbauwand	RD	Rohfußboden
	LD	Rohdecke
	FD	Fertigdecke
	LH	Lichte Höhe
	BRH	Brüstungshöhe ab OK RFB
	RR	Regenfallrohr
	LR	Leerrohr
	DO	Deckendurchbruch
	BD	Bodendurchbruch
	BE	Bodeneinlauf
	WD	Wanddurchbruch
GK- Vorwand raumhoch (GIS)	DS	Deckenschlitz
	BE	Bodeneinlauf
GK- Vorwand 1,20 m (GIS)	WWS	Waagerechter Wandschlitz
	SWS	Senkrechter Wandschlitz
	FS	Fußbodenschlitz
	AS	Aussparung
	GR	Gurtrollen
	VM	Vormauerung
	BK	Bodenkanal
	KB	Kernbohrung
Dämmung hart		
Dämmung weich		
Abdichtung		
Schotter		
Kies		
Spült		
Wanddurchbruch		
Decken-Bodendurchbruch		

UK	Unterkannte
OK	Oberkannte
RFB	Fertigfußboden
RD	Rohfußboden
LD	Rohdecke
FD	Fertigdecke
LH	Lichte Höhe
BRH	Brüstungshöhe ab OK RFB
RR	Regenfallrohr
LR	Leerrohr
DO	Deckendurchbruch
BD	Bodendurchbruch
BE	Bodeneinlauf
WD	Wanddurchbruch
DS	Deckenschlitz
BE	Bodeneinlauf
WWS	Waagerechter Wandschlitz
SWS	Senkrechter Wandschlitz
FS	Fußbodenschlitz
AS	Aussparung
GR	Gurtrollen
VM	Vormauerung
BK	Bodenkanal
KB	Kernbohrung

T30-180	Feuerschutzabschlüsse (Feuerschutztüren/-tore)
G30-180	Feuerschutzabschlüsse (Feuerschutzfenster)
F30-180	sonstige feuerwiderstandsfähige Teile
RS	Rauchschuttfunktion

G	Glas
HZ	Heizung
E	Elektro
S	Sanitär

ESG	Einscheibensicherheitsglas
VSG	Verbundsicherheitsglas
R 10	Rutschsicherheit

Bodenbelagswechsel	
Höhenkote Fertigmaß	
Höhenkote Rohbaumaß	
Detailverweis	D 001
Türnummern	
Fensternummern	


T = Tür	Geschoss Art	Anzahl
F = Fenster	1 = 1.OG	1 = 1.OG
	2 = 2.OG	2 = 2.OG
	3 = 3.OG	3 = 3.OG
	4 = 4.OG	4 = 4.OG
	5 = 5.OG	5 = 5.OG

Wandaufbau Außenwände

Außenwände KS-WDVS
15 mm Außenputz
140 mm Dämmung
5 mm Kleberschicht
200 mm Kalksandstein

Außenwände STB-WDVS
15 mm Außenputz
140 mm Dämmung
5 mm Kleberschicht
200 mm Stahlbeton

G	F	E	D	C	B	A
24.03.2020	MB	Gebäude an TG angepasst				
17.01.2020	MB	Erstellt				
Index	Datum	Name	Änderungen/Ergänzungen/Stand			

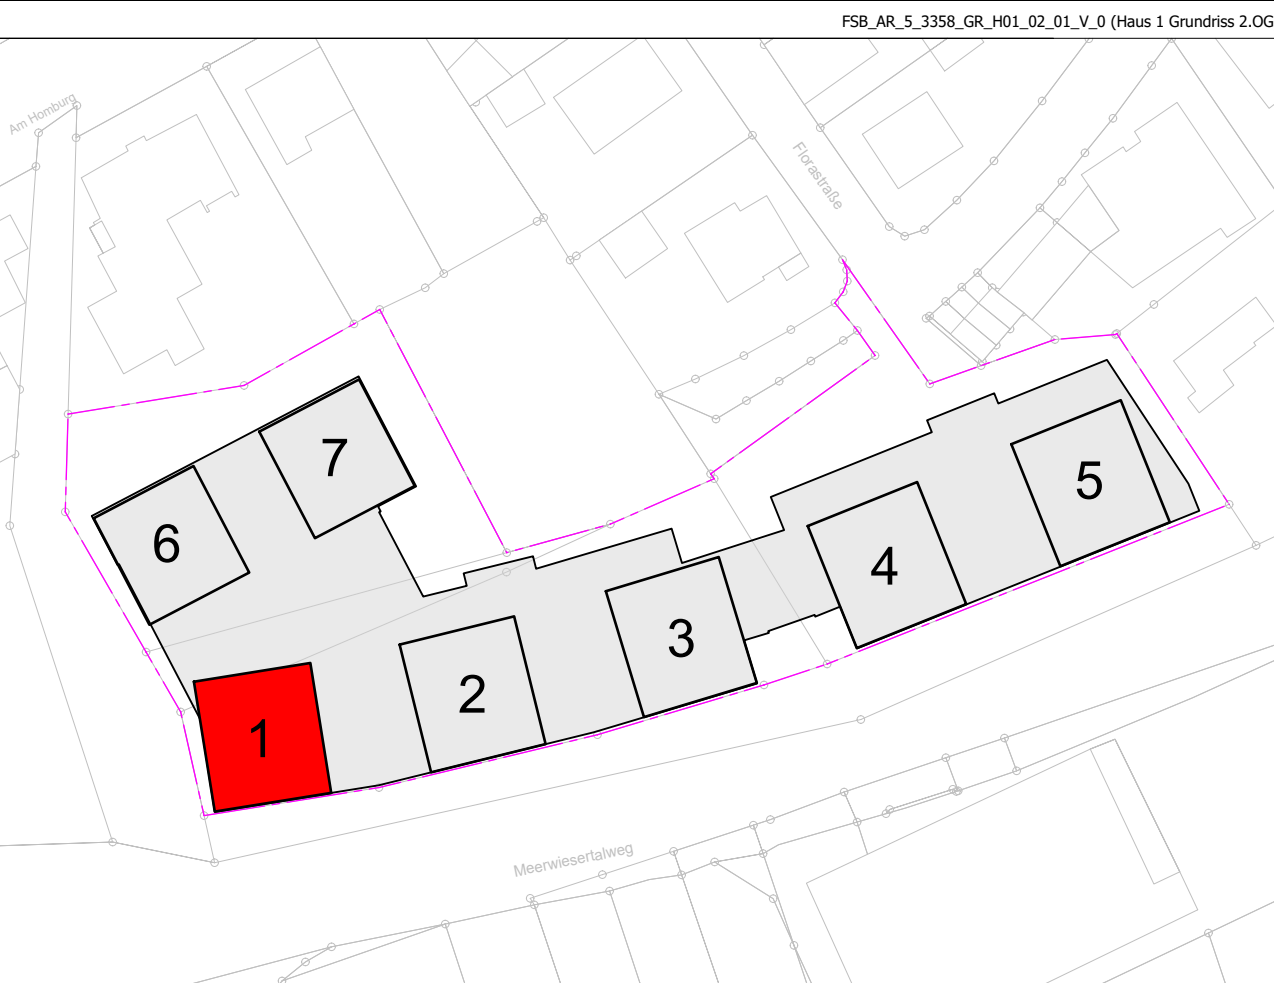

ARCHITEKT

BAUERLE architekten+brandschutz

Heinrich-Barth-Straße 20
D - 66 115 Saarbrücken
Tel.: +49(0)631 - 844 931-0
Fax: +49(0)631 - 844 931-18
info@bauerle-architekten-brandschutz.de
www.bauerle-architekten-brandschutz.de

BAUHERR

THOR Zweite GmbH & Co. KG
Herr Thomas Schulze-Wischeler
Ulmestraße 22
60325 Frankfurt am Main

PROJEKT

206-18_WP_Florapark_SB
Meerwerderstraße 4a, 4b, 4c, 6, 6a
Florastraße 8, 10
66123 Saarbrücken

Gemarkung	Flur	Flurstück
St. Johann	30	49/9; 49/8; 50/2; 46/7

Erstellt	Gedruckt	Maßstab
17.01.2020	24.03.2020	1:50

WERKPLANUNG

FSB_AR_5_3358_GR_H01_02_01_V_0 (Haus 1 Grundriss 2.OG)